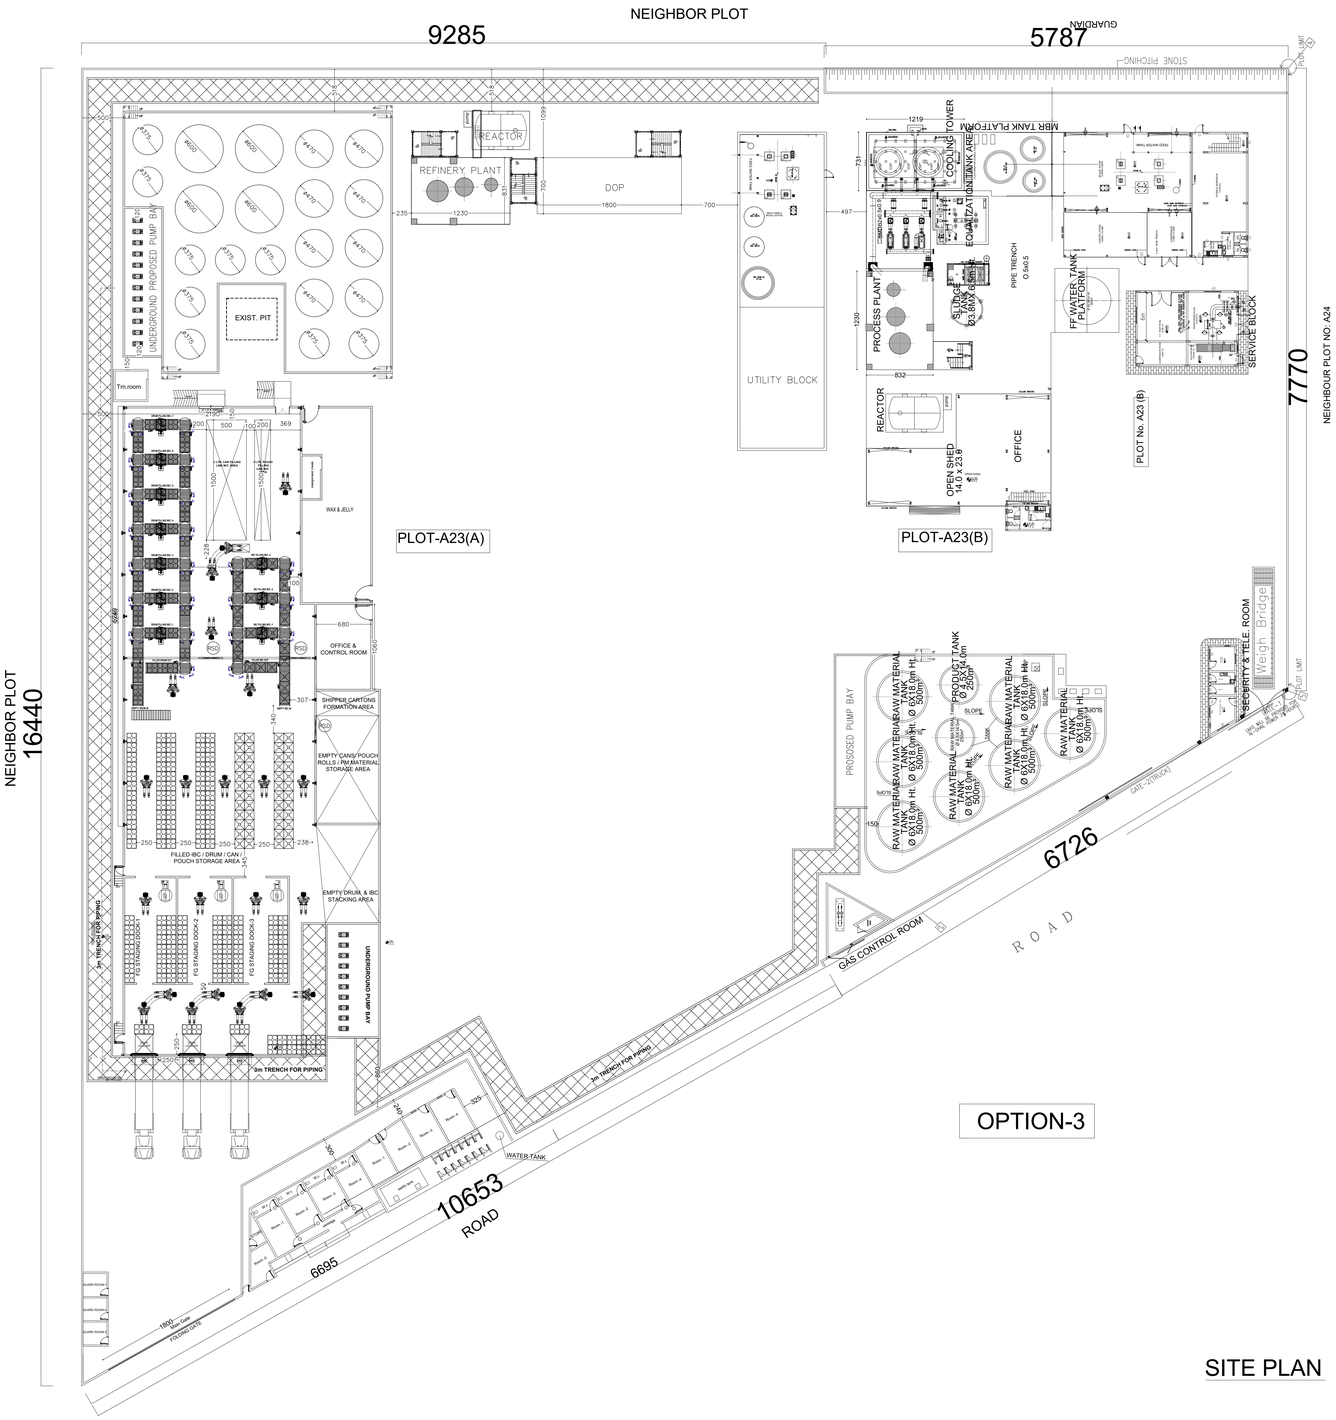

SITE PLAN

AREA STATEMENT						
TOTAL PLOT AREA: 5000.0 m²						
S/N	AREA DESCRIPTION	Ground Flr. Area (m²)	First. Flr./ Area (m²)	Second Flr. Area (m²)	Roof Flr. Area (m²)	Total Area (m²)
01	PROPOSED OPEN SHED EXTENSION	847.00	-	-	-	847.00

GENERAL NOTES:

1. ALL DIMENSIONS ARE IN CENTIMETERS (CM) AND LEVELS ARE IN METERS (M) UNLESS OTHERWISE SPECIFIED.
2. DO NOT SCALE FROM THE DRAWING.
3. ALL DIMENSIONS ARE TO BE VERIFIED.
4. THESE DRAWINGS SHALL BE READ IN CONJUNCTION WITH RELEVANT ARCHITECTURAL, M.E.P. DETAILS AND SPECIFICATIONS. CONTRACTOR SHALL COORDINATE THESE DRAWINGS AND REPORT IF THERE ARE ANY DISCREPANCIES FOR CLARIFICATION BEFORE PROCEEDING WITH THE WORK.
5. ALL LEVELS IN THE SETTING OUT PLAN ARE TENTATIVELY SHOWN. ACTUAL LEVELS HAVE TO BE DECIDED AT THE PROJECT SITE BY THE CONTRACTOR AND SHALL BE BROUGHT TO THE ATTENTION OF THE CONSULTANT.
6. SHOP DRAWINGS ARE TO BE SUBMITTED BEFORE EXECUTION OF WORK ON SITE.
7. THE CONTRACTOR IS THE ONLY PARTY RESPONSIBLE FOR ANY WORK CARRIED OUT ON SITE WITHOUT THE CONSULTANT'S KNOWLEDGE.
8. DRAINAGE SYSTEM AND WATER SUPPLY SYSTEM HAVE TO BE EXECUTED AS PER THE SITE CONDITION BY THE CONTRACTOR.

Client	ASIA PETROCHEMICALS LLC			Plot No.	PLA-23A
Project	FACTORY SHED,ACCOMMODATION AND SERVICE BLOCKS			Block No.	
Drg.Title	SITE PLAN-CONCEPT			Job No.	217
Area	AL HAMRA INDUSTRIAL ZONE			Revision No.	
G.Manager	ENG.BADR	Project Manager	ENG.KISHOR	Draw. Type.	ARCH
Architect	ENG.HALA	Elec. Engr.	ENG.EHSAN	Sht. No.	A01
Site Eng.	ENG.KISHOR	F.F. / F.A. Engr.	ENG.EHSAN	Scale	1:100
Strc. Eng.	ENG.HAFIZ	Drawn by	ENG.HALA	Date	25-09-2024

GENERAL MANAGER
ENG.BADHURDEEN
MOBILE No: 055 478 5834

مدير عام
م . بـدر الـدين
MOBILE No: 055 478 5834

Modern
مـــودرن للإستشـــارات الهندســـية
Modern Engineering Consultants
JULPHAR TOWER -OFFICE TOWER ,FLOOR - 5 - FLAT NO : 501
RAS AL KAIMAH - UAE - TEL : 07 2666688
EMAIL : info.mdrn501@gmail.com